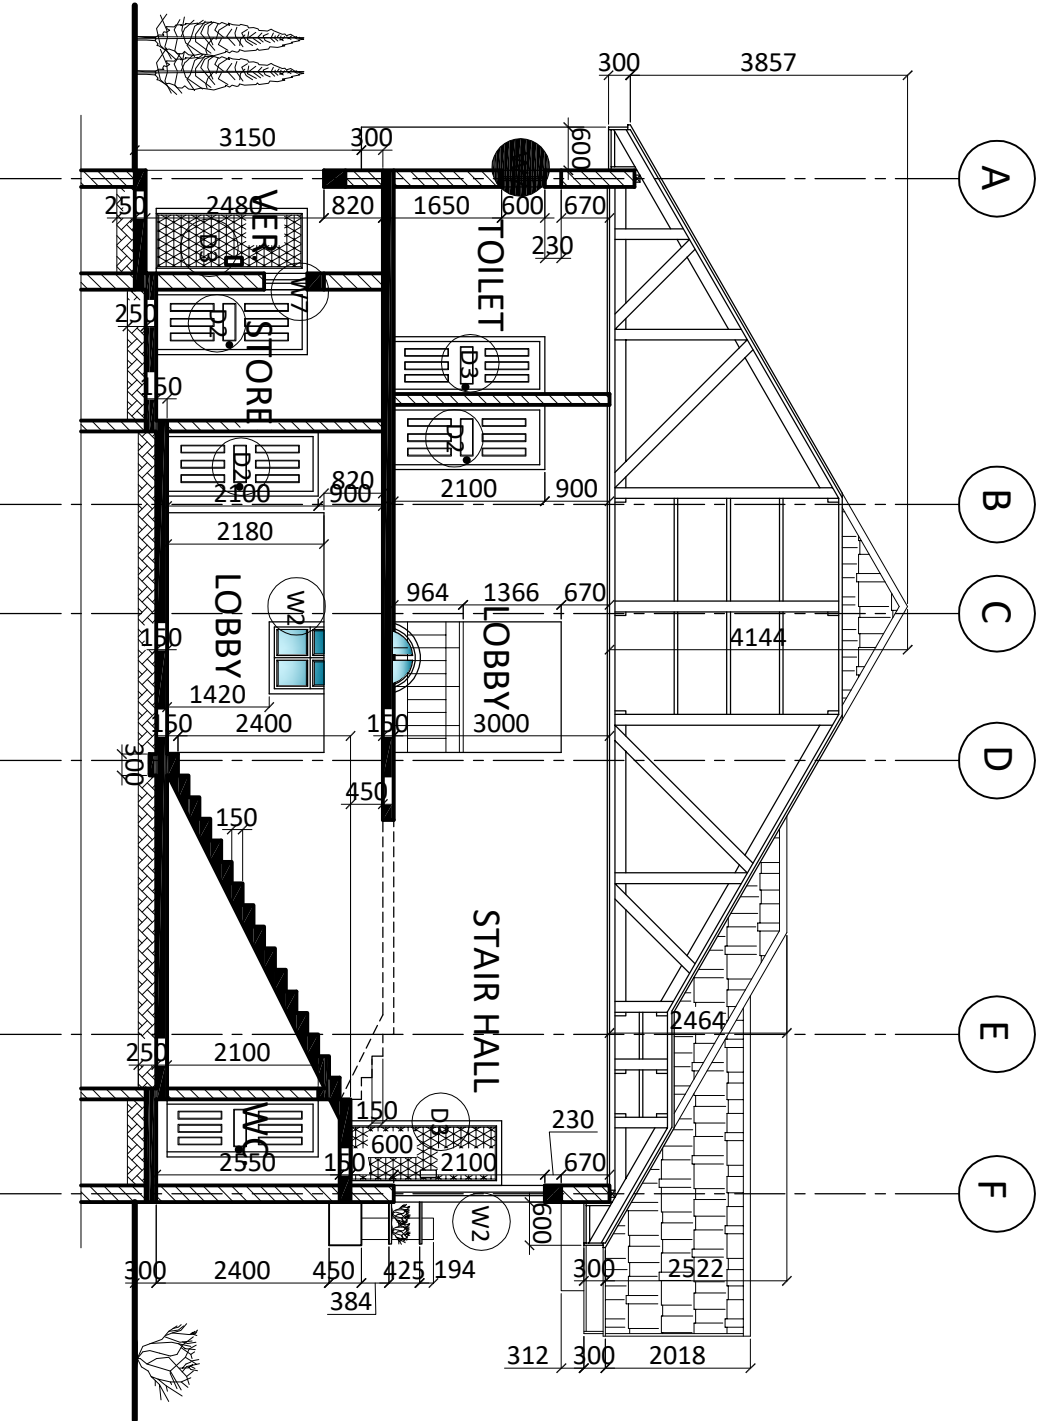




SECTION NOTES

a) ROOF

- *0.55mm guage long span aluminium roofing sheets and ridge capping;
- *50x75mm hardwood purlins @900mm centers;
- *50x150mm hardwood rafters @1200mm centers;
- *50x150mm hardwood struts @ 1200mm centers;
- *50x150mm hardwood tiebeams @1200mm centers;
- 100x75mm hardwood wallplates;
- *50x50mm hardwood noggings @1200mm centers.

SECTION NOTES

b) FLOOR

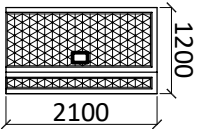
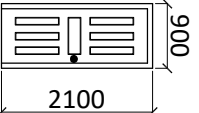
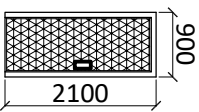
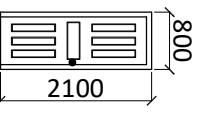
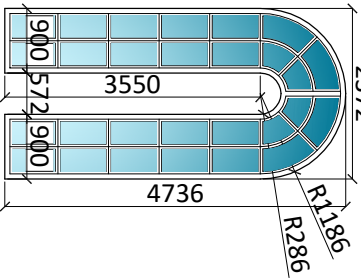
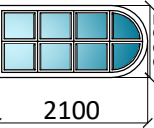
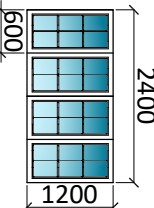
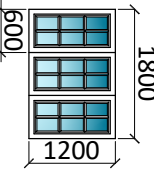
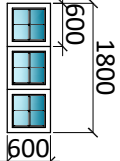
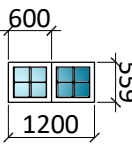
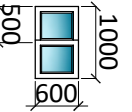
- *150mm thick concrete floor bed on;
- *200mm thick well consolidated hardcore filling.
- * note : refer to structural drawings for details of foundation.

SECTION NOTES

c) STAIRS

- *150mm risers
- *300mm treaders
- *275mm waist

SECTION X - X (scale 1 : 100)

DOORS AND WINDOWS SCHEDULE						
						
D1 steel security door 01 nos.		D2 wrought H/W panel door 14 nos.		D3 double panel steel door 02 nos.		D4 wrought H/W panel door 09 nos.
						
W1 aluminium curtain wall 01 nos.	W2 aluminium curtain wall 01 nos.	W3 casement swing window 01 nos.	W4 ditto 11 nos.	W5 casement swing window 01 nos.	W6 casement projected window 01 nos.	W7 casement swing window 12 nos.